


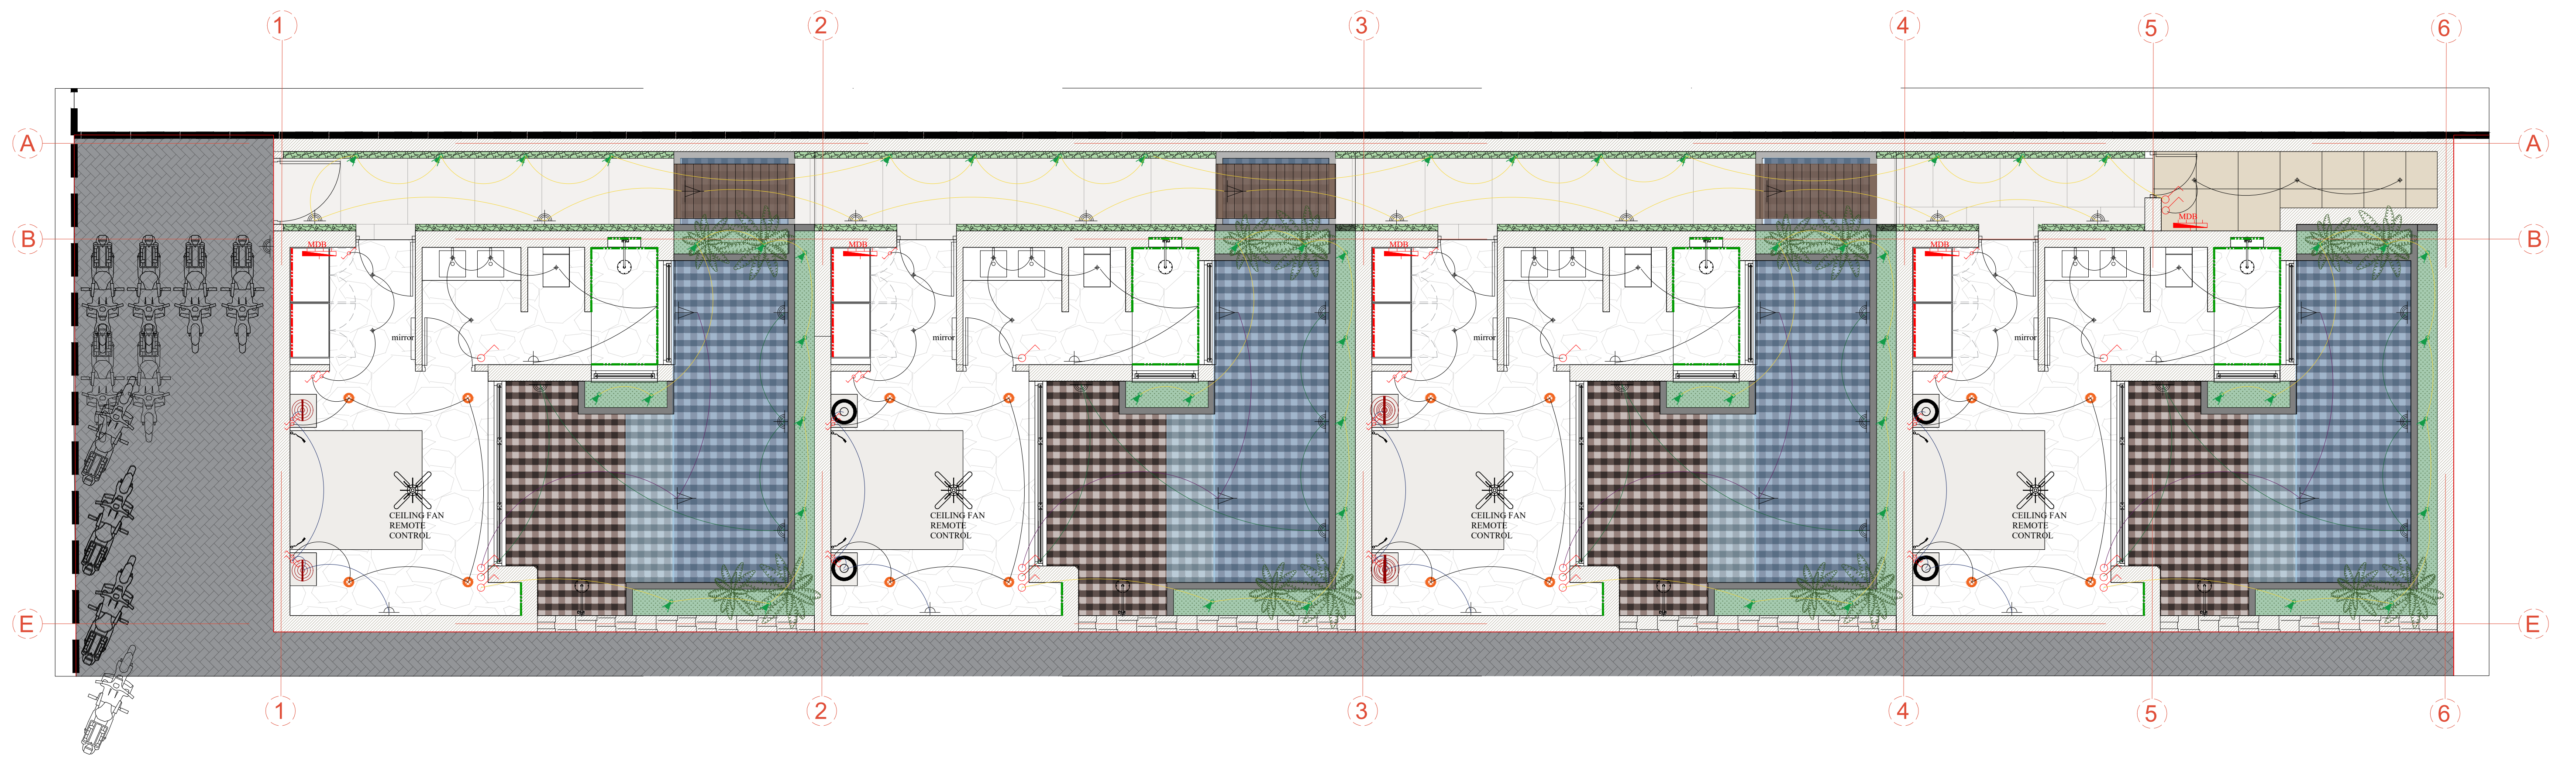

GENERAL LAYOUT LIGHTING

LEGEND – ELECTRICAL INSTALLATION	
	Single switch
	Single pole, two-way switch (SPDT)
	Waterproof single switch – IP65
	Recessed ceiling spotlight
	Recessed ceiling spotlight for beams
	Wall light
	Table lamp
	Ceiling lamp
	Wall reading light
	LED strip lighting inside cabinet
	LED strip lighting – floor / countertop / underside
	Step recessed spotlight – exterior
	Outdoor wall light
	Underwater LED spotlight
	Outdoor wall light
	Main Distribution Board (MDB)

BOUTIQUE HOTEL - FH NY (NAME TBC)			
LOCATION	NYANG NYANG	REVISION	REV_00
CLIENT	RIGI	DATE	12/01/2026
SHEET TITLE	ELECTRICITY - LIGHTING	SCALE	1/100 @ A3 1/50 @ A1
INTERIOR ARCHITECT		SHEET NUMBER	
M A R M A R ARCHITECTURE & INTERIOR DESIGN hello@marmar-studio.net +62 812 2784 7931 @marmarstudiobali		06.00	