



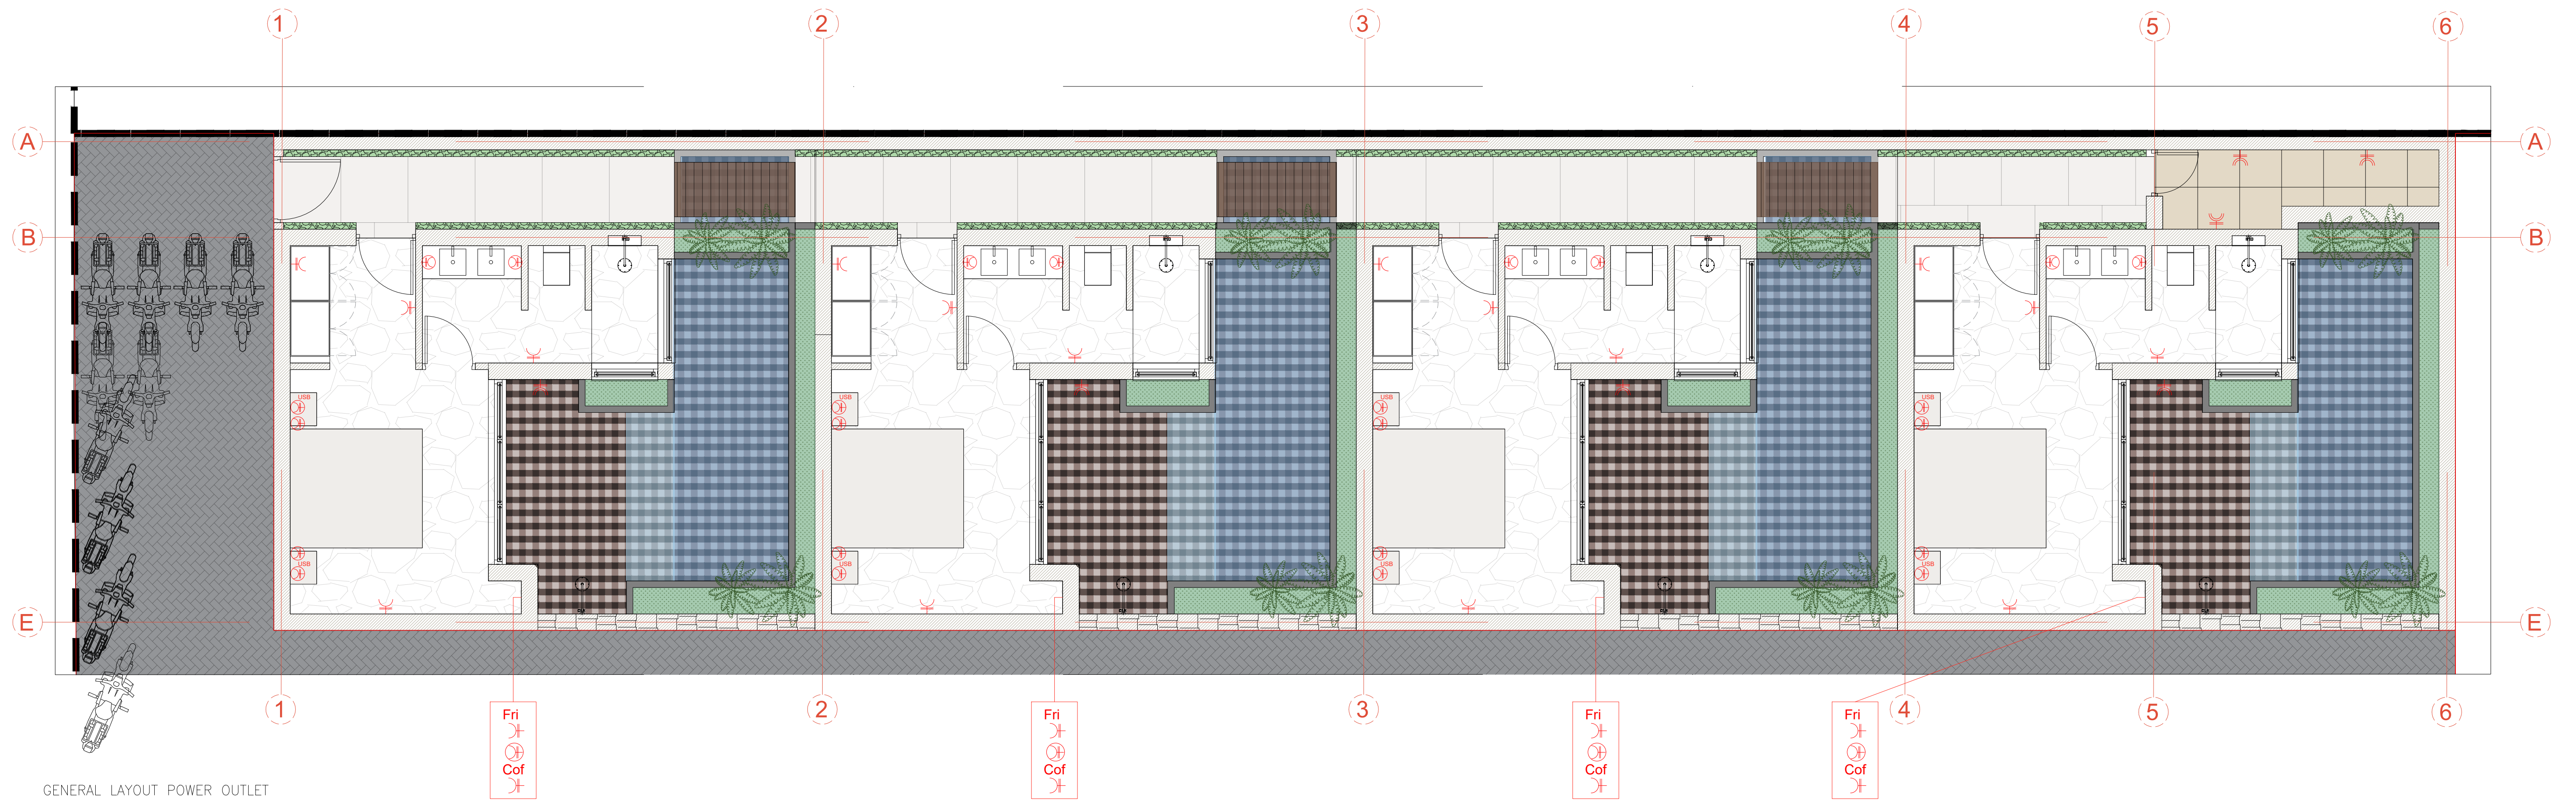

GENERAL LAYOUT POWER OUTLET

GENERAL DIMENSIONS

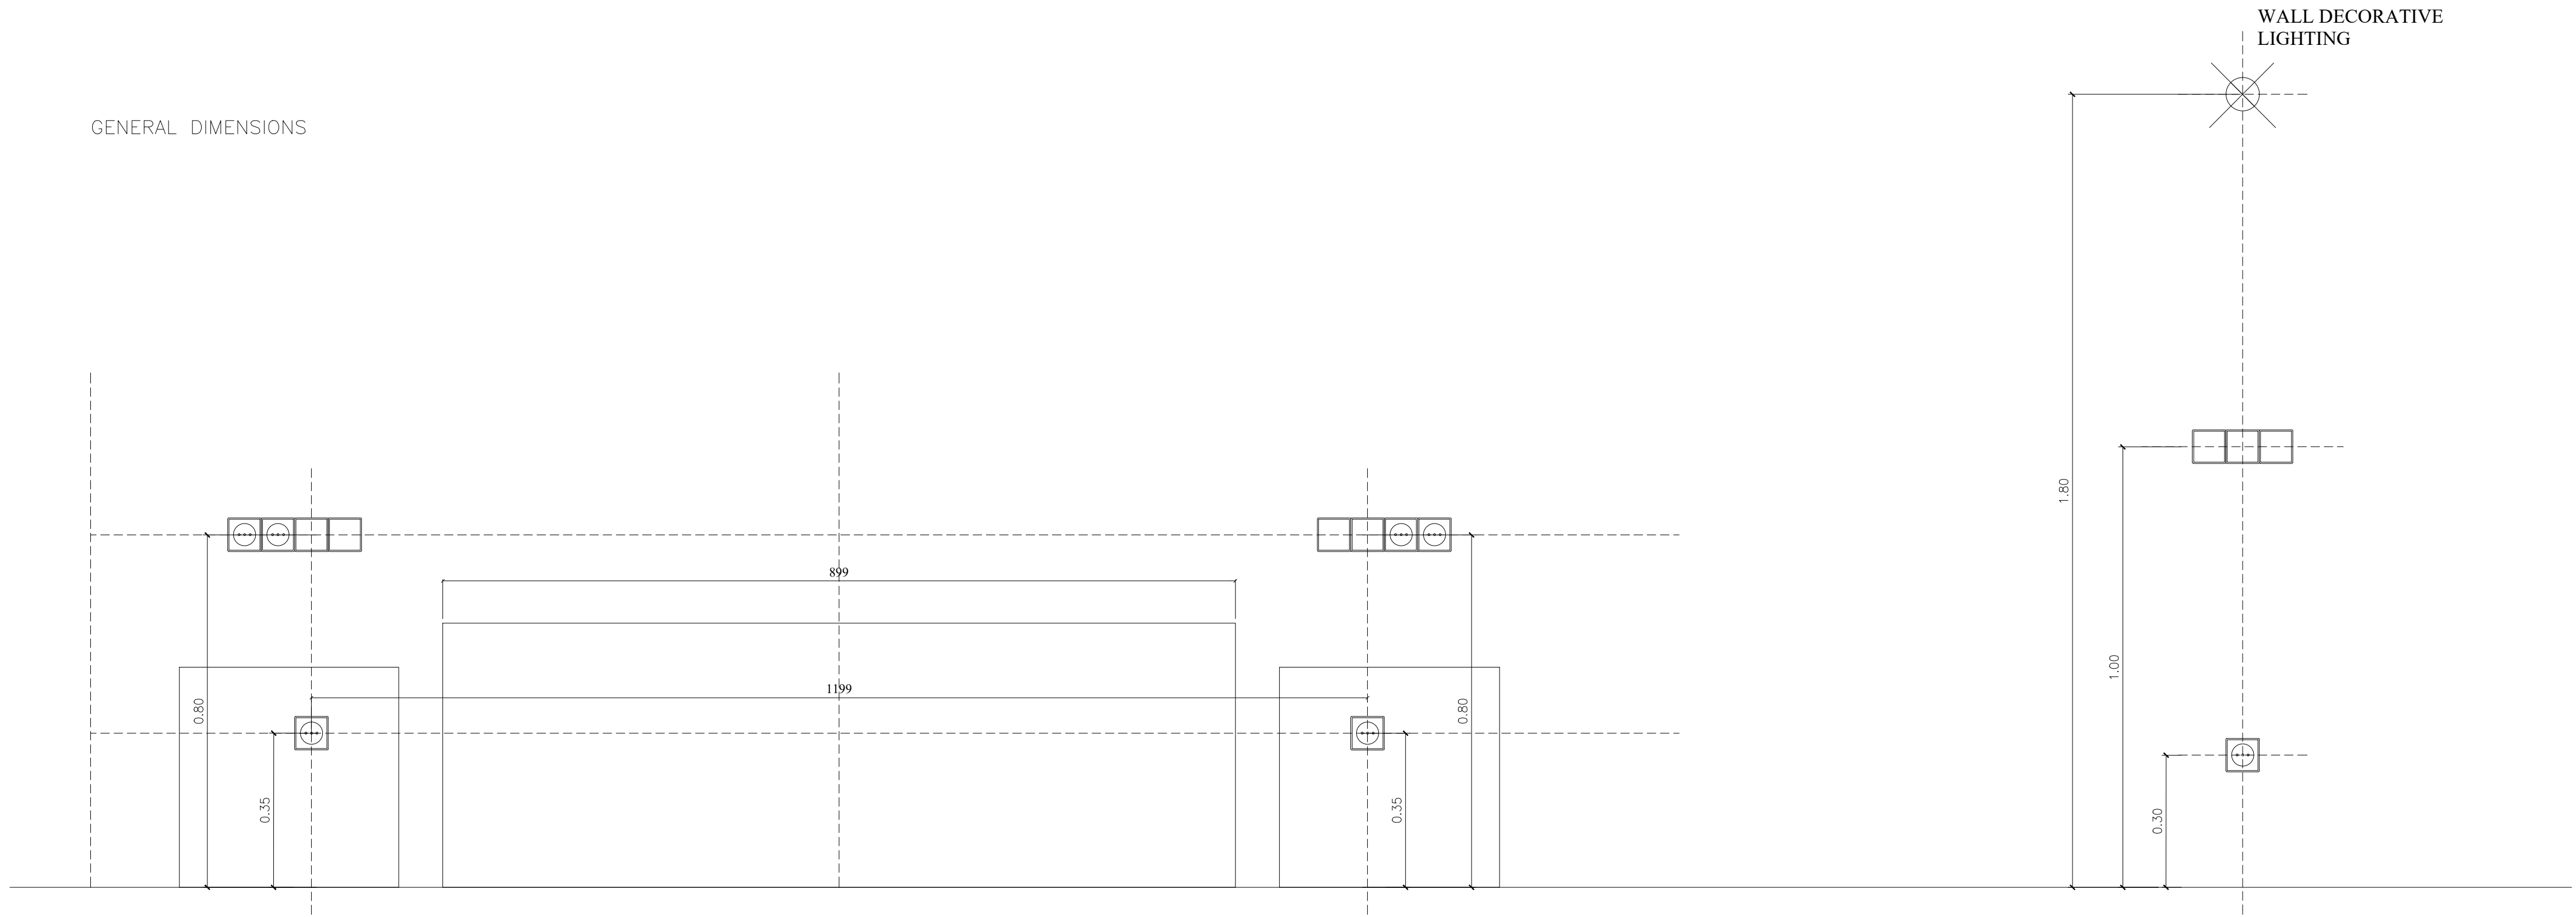

LEGEND – ELECTRICAL INSTALLATION / POWER OUTLETS	
	Single switch
	Single pole, two-way switch (SPDT)
	Waterproof single switch – IP65
	2P+E 16A power outlet for general use, low position
	2P+E 16A power outlet for general use, high position
	2P+E 16A power outlet for general use, high position
	2P+E 16A waterproof power outlet for general use
	Doorbell push button
	2P+E 16A power outlet for WASHING MACHINE
	Outlet 16A 2P+E – FRIDGE
	Outlet 16A 2P+E – COFFEE
	Main Distribution Board (MDB)

BOUTIQUE HOTEL - FH NY (NAME TBC)			
LOCATION	NYANG NYANG	REVISION	REV_00
CLIENT	RIGI	DATE	12/01/2026
SHEET TITLE	ELECTRICITY - POWER OUTLET	SCALE	1/100 @ A3 1/50 @ A1
INTERIOR ARCHITECT		SHEET NUMBER	
M A R M A R ARCHITECTURE & INTERIOR DESIGN		06.01	
hello@marmar-studio.net +62 812 2784 7931 @marmarstudiobali			